


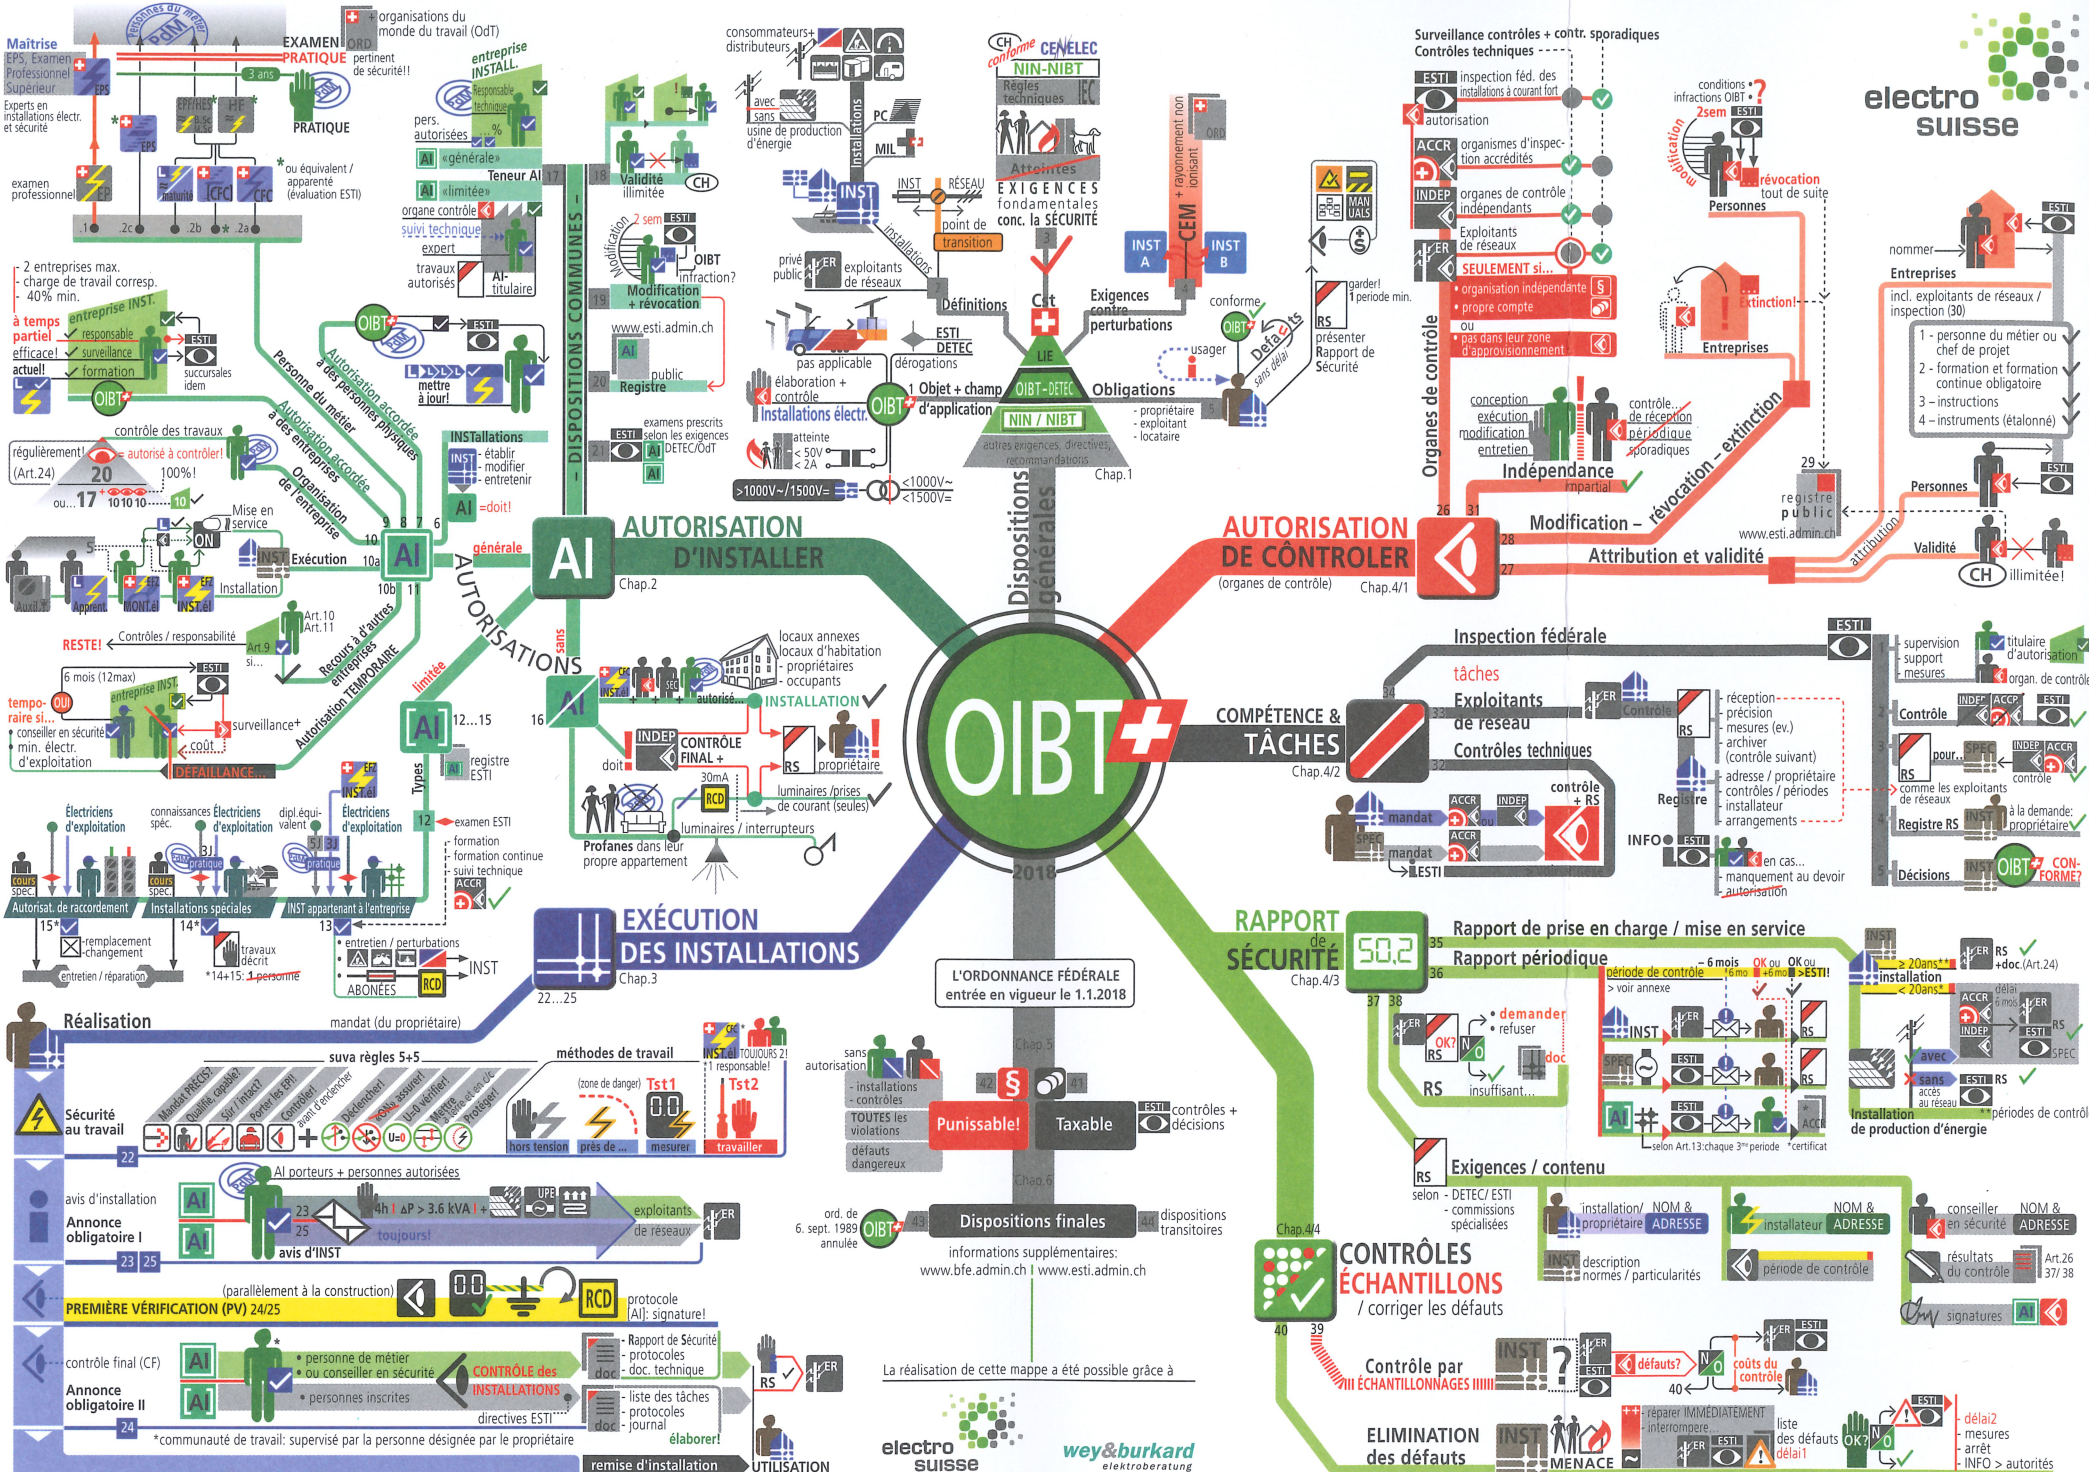

	1	3	5	10	20
Installations fédérales - installations de transport par conduites soumises à la surveillance de la confédération					
Installations militaires - magasins de munitions souterrain, classifié - dépôts de carburants souterrains classifiés - casernes - arsenaux - constructions de protection civile - constructions de protection civile avec IPE ou protection NEMP					
Chemins de fer - voies ferrées, tunnel, ateliers et installations de nettoyage - toutes les autres					
Routes nationales de catégorie 1 et 2					
Bateaux - bateaux sport / de plaisance - bateaux pour le transport commercial de passagers / de marchandises - campings et embarcadères					
Autorisations limitée - autorisations pour électriciens d'exploitation [Art. 13] - autorisation pour installations spéciales [Art. 14] - autorisation de raccordement [Art. 15]					
Sites des marchés de construction					
Ateliers - locaux industriels et commerciaux / grands commerces - locaux soumis à la corrosion - laboratoires et locaux d'essais - stations de recharge publiques pour les véhicules électriques - install. HT alim. par des install. BT à l'exception des éclairages au néon et des install. à rayons X à usage non médical - locaux commerciaux inflammables ou humides - ateliers commerciaux et de réparation					
Bâtiments avec une accumulation de personnes - cinéma, théâtre, danse, maison de repos / d'enfants / d'asile, hôpitaux - jardins d'enfants, écoles et hautes écoles - grands magasins, restaurant et hôtel - salles d'expositions - boutique, kiosque, bistros, Take Away (<1200m ² / Capacité <300 personnes) - musées, églises - bureaux, banques, assurances					
Différentes installations - locaux où sont fabriqués, traités ou entreposés des explosifs ou des produits pyrotechniques - mines - piscines intérieure et extérieure, stations d'épuration des eaux usées - ouvrages souterrains, tunnels, cavernes - installations ou parties d'installations en schéma III - IPE en ilôt					
Ex-Zones - 0 et 1, 20 et 21 - 2 et 22 dépôts de carburants - 0 et 1 dans les stations d'essence et les ateliers de réparations des automobiles - 2 et 22					
Locaux à usage médicaux... - massage - chambres, locaux d'examen ou de traitement, hydro-, physiothérapie - hémodialyse, cabinets dentaires - accouchement, ECG/EEG/EHG, endoscopie, urologie - IRM, radiodiagnostic/traitement, médecine nucléaire - IRM, anesthésie, préparation aux OP's, pose de plâtres, salles d'OP - réveil, cathétérisme cardiaque, soins intensifs, angiographie - enfants prématurés, soins intermédiaires (IMCU)					
Agriculture et l'horticulture - bâtiments résidentiels - étable et grange					
Immeubles d'habitation					
Changement de propriétaire (si le dernier contrôle effectué date de 5 ans)					
Installations de téléphonie mobile sur des mâts HT Alimentations photovoltaïques (contrôle comme la maison/l'immeuble qui va avec)					



Ordonnance sur les installations à basse tension

SR 734.27



Pour plus de sécurité: Vérifications - essais - mesures (chap. 6.1.2...4)

Vérifications (6.1.2 Examen visuel)



a) Équipement

- approprié pour l'espace
- selon les exigences IP
- accessibilité
- facilité d'exploitation
- conformément à la doc. du fabricant
- marquage / approbations disponibles

b) Dispositifs de sectionnement, de coupure et de protection

- choix (y compris IP)
- disposition
- réglages

c) Mesures de protection

- contact direct (distances, barrières, enveloppes)
- effets thermiques
- cloisons de protection contre les incendies

d) Canalisations

- conducteurs
- barres

- choix / dimensionnement
- pose
- connexions (dimensionnement / pas de desserrage)
- identification / affectation
- identification PE - PEN - N

e) Documentation

- marquage et signes d'essais requis
- marquages et affectation (canalisations et équipements)
- plans et schémas
- symboles d'avertissement et panneaux d'interdiction
- indications et marques
- modes d'emploi

Essais (6.1.3.1 généralités)



- personnes
- animaux
- choses

a) Équipement de surveillance

- Isolation
- disjoncteur différentiel (RCD)
- > bouton de test

b) Équipement de protection


- annonces
- signalisations

c) Fonctions de sécurité


- arrêt d'urgence / stop d'urgence
- dispositif de blocage
- source d'alimentation de sécurité
- alimentation sans coupure ASC
- éclairage de sécurité

Mesures

a) Test de conducteur de protection et des liaisons équipotentielles de protection

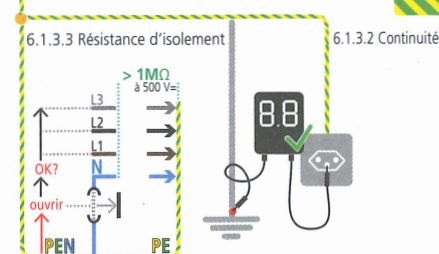


b) Coupure automatique (6.1.3.6)

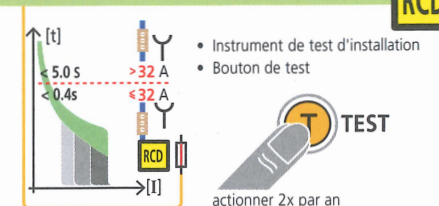


c) Polarité et ordre de phases

6.1.3.8. Installation 6.1.3.9 Champ tournant

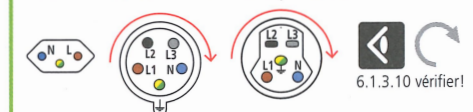

d) Catégories de mesure I...IV (EN 61010-01)

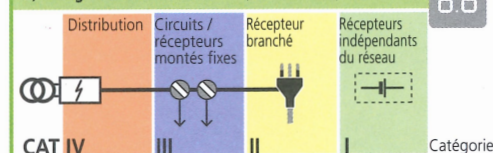

e) Enregistrer les résultats / préparer les documents

- 6.1.4 Documentation
- Rapport de Sécurité
- protocoles
- documentation technique
- schémas
- ...

Pour... Information / documentation

- Formation / certification
- Expertise

www.electrosuisse.ch



- Conseils pratiques
- Dossier de sécurité
- Formation sur place

www.elektroberatung.ch

